WA12 · Fenstervorschlag EG

Raumbezogen, geradlinig und auf die Formate von WA14 abgestimmt



Blau = neue Öffnung als Vorschlag. Der bestehende Hauseingang bleibt erhalten. Die Grundrissaufteilung wird nicht geändert.


Nr. / Raum	B × H	UK
01 · WE1 Wohnen	1.09 × 2.15	0.15
02 · WE1 Essen / Terrasse	2.40 × 2.30	0.00
03 · WE1 Schlafen	1.09 × 2.15	0.15
04 · WE1 DU/WC	0.74 × 1.10	1.20
05 · WE1 Zimmer 1	1.09 × 2.15	0.15
06 · Gehhilfenraum	0.74 × 1.10	1.20
07 · Treppenhaus / Flur	1.09 × 1.10	1.20
08 · Technik	0.74 × 1.10	1.20
09 · Technik	0.74 × 1.10	1.20

Gestaltungsregel: 1,09 m für stehende Wohn-/Schlafraumfenster; 0,74 m für kleine, meist hochliegende Öffnungen; 2,40 / 2,99 m für breite Wohn- und Terrassenöffnungen. Gemeinsame Oberkanten: EG/OG 2,30 m, PH 2,40 m.

Grundrissbezug: Die Fenster berücksichtigen Bettstellwand, Küchenzeile und Sanitärobjekte. Abstellräume werden nicht pauschal verglast. Treppenhaus- und Technikfenster sind funktionale Vorschläge; Lüftung und Treppenschnitt sind abzustimmen.

WA12 · Fenstervorschlag OG

Raumbezogen, geradlinig und auf die Formate von WA14 abgestimmt

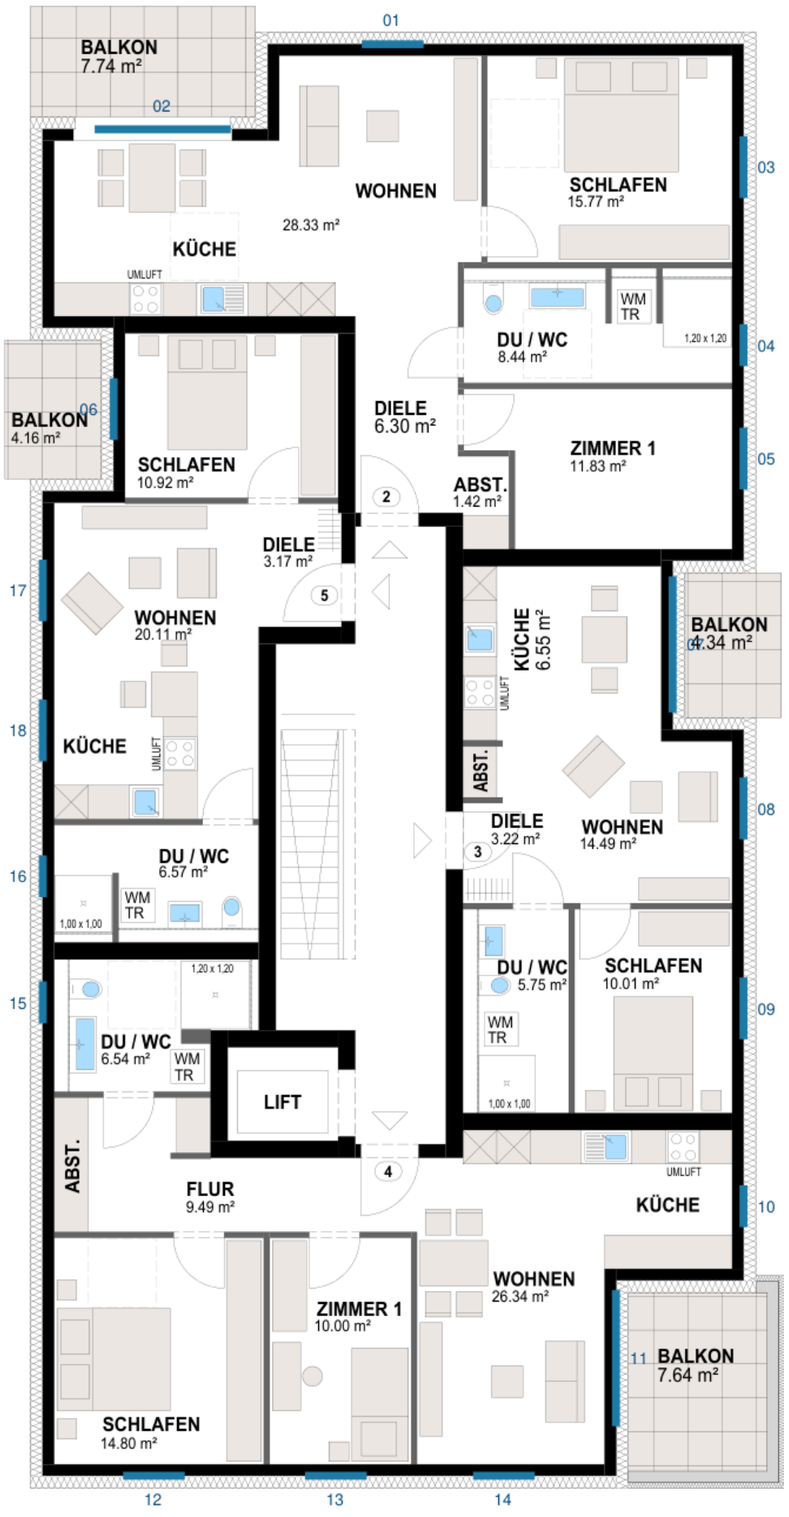

Blau = neue Öffnung als Vorschlag. Der bestehende Hauseingang bleibt erhalten. Die Grundrissaufteilung wird nicht geändert.


Nr. / Raum	B × H	UK
01 · WE2 Wohnen	1.09 × 2.15	0.15
02 · WE2 Wohnen / Balkon Nord	2.40 × 2.30	0.00
03 · WE2 Schlafen groß	1.09 × 2.15	0.15
04 · WE2 DU/WC	0.74 × 1.10	1.20
05 · WE2 Zimmer 1	1.09 × 2.15	0.15
06 · WE2 Schlafen klein / Balkon	1.09 × 2.30	0.00
07 · WE3 Küche/Essen / Balkon	2.40 × 2.30	0.00
08 · WE3 Wohnen	1.09 × 2.15	0.15
09 · WE3 Schlafen	1.09 × 2.15	0.15
10 · WE4 Küche	0.74 × 1.10	1.20
11 · WE4 Wohnen / Balkon Süd	2.40 × 2.30	0.00
12 · WE4 Schlafen	1.09 × 2.15	0.15
13 · WE4 Zimmer 1	1.09 × 2.15	0.15
14 · WE4 Wohnen	1.09 × 2.15	0.15
15 · WE4 DU/WC	0.74 × 1.10	1.20
16 · WE5 DU/WC	0.74 × 1.10	1.20
17 · WE5 Wohnen	1.09 × 2.15	0.15
18 · WE5 Wohnen/Küche	1.09 × 2.15	0.15

Gestaltungsregel: 1,09 m für stehende Wohn-/Schlafraumfenster; 0,74 m für kleine, meist hochliegende Öffnungen; 2,40 / 2,99 m für breite Wohn- und Terrassenöffnungen. Gemeinsame Oberkanten: EG/OG 2,30 m, PH 2,40 m.

Grundrissbezug: WE2 erhält beide im Grundriss vorgesehenen Balkonzugänge, WE3 und WE4 jeweils einen. Das Bad von WE3 liegt innen und erhält kein Außenfenster. WE5 wird über zwei gleiche stehende Fenster belichtet. Ein rechnerischer Belichtungsnachweis ist nicht Bestandteil.

WA12 · Fenstervorschlag PH

Raumbezogen, geradlinig und auf die Formate von WA14 abgestimmt

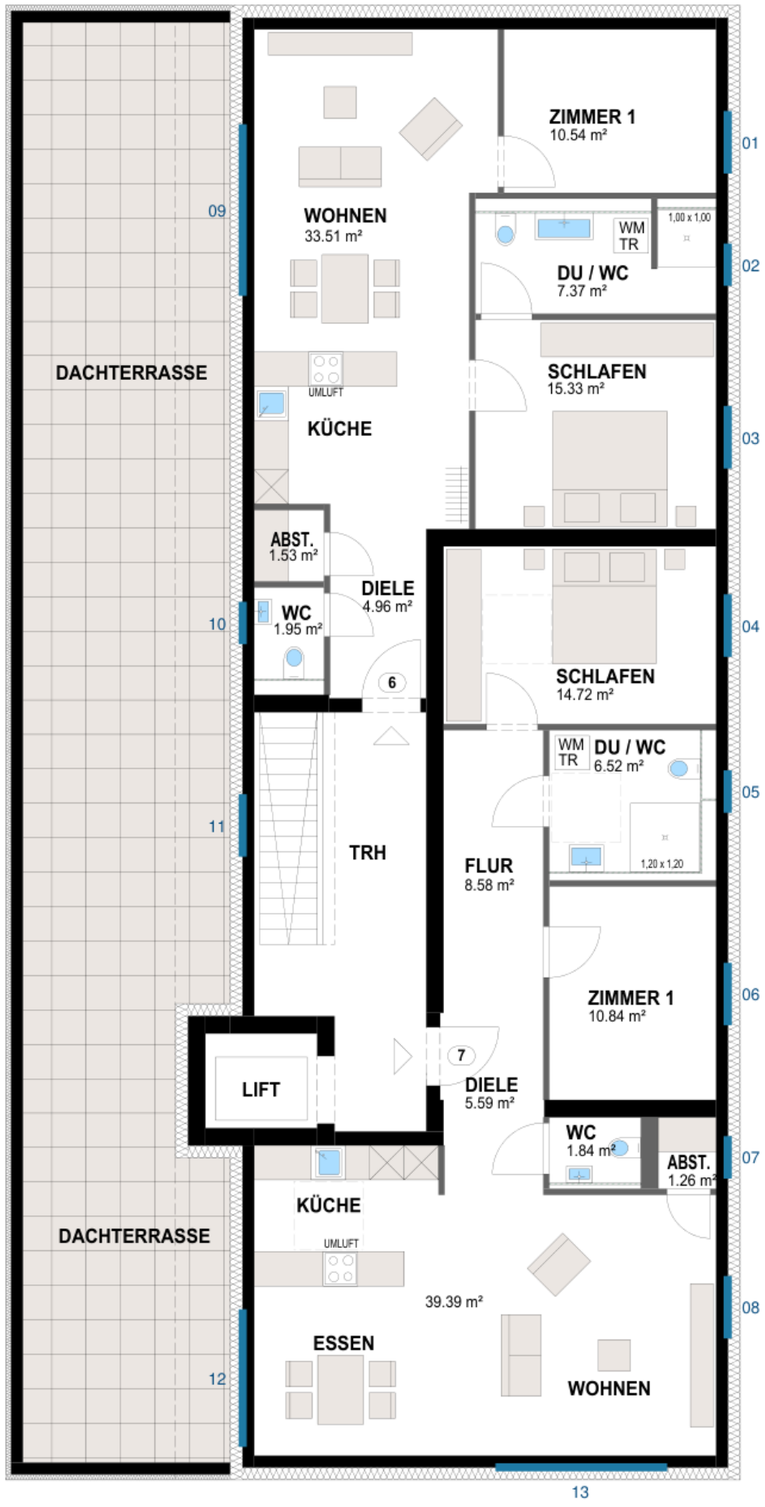

Blau = neue Öffnung als Vorschlag. Der bestehende Hauseingang bleibt erhalten. Die Grundrissaufteilung wird nicht geändert.

Nr. / Raum	B × H	UK
01 · WE6 Zimmer 1	1.09 × 2.25	0.15
02 · WE6 DU/WC	0.74 × 1.20	1.20
03 · WE6 Schlafen	1.09 × 2.25	0.15
04 · WE7 Schlafen	1.09 × 2.25	0.15
05 · WE7 DU/WC	0.74 × 1.20	1.20
06 · WE7 Zimmer 1	1.09 × 2.25	0.15
07 · WE7 Abstellraum	0.74 × 1.20	1.20
08 · WE7 Wohnen	1.09 × 2.25	0.15
09 · WE6 Wohnen / Dachterrasse	2.99 × 2.40	0.00
10 · WE6 WC	0.74 × 1.20	1.20
11 · Treppenhaus PH	1.09 × 1.20	1.20
12 · WE7 Essen / Dachterrasse	2.40 × 2.40	0.00
13 · WE7 Wohnen Süd	2.99 × 2.25	0.15

Gestaltungsregel: 1,09 m für stehende Wohn-/Schlafraumfenster; 0,74 m für kleine, meist hochliegende Öffnungen; 2,40 / 2,99 m für breite Wohn- und Terrassenöffnungen. Gemeinsame Oberkanten: EG/OG 2,30 m, PH 2,40 m.

Grundrissbezug: Beide Wohnungen erhalten einen direkten Dachterrassenzugang außerhalb der Küchenzeilen. Das WC von WE7 liegt innen; Öffnung 07 gehört zum außenliegenden Abstellraum. Fenster an der Treppe sind nach dem Schnitt zu prüfen.